


窗户



单扇门

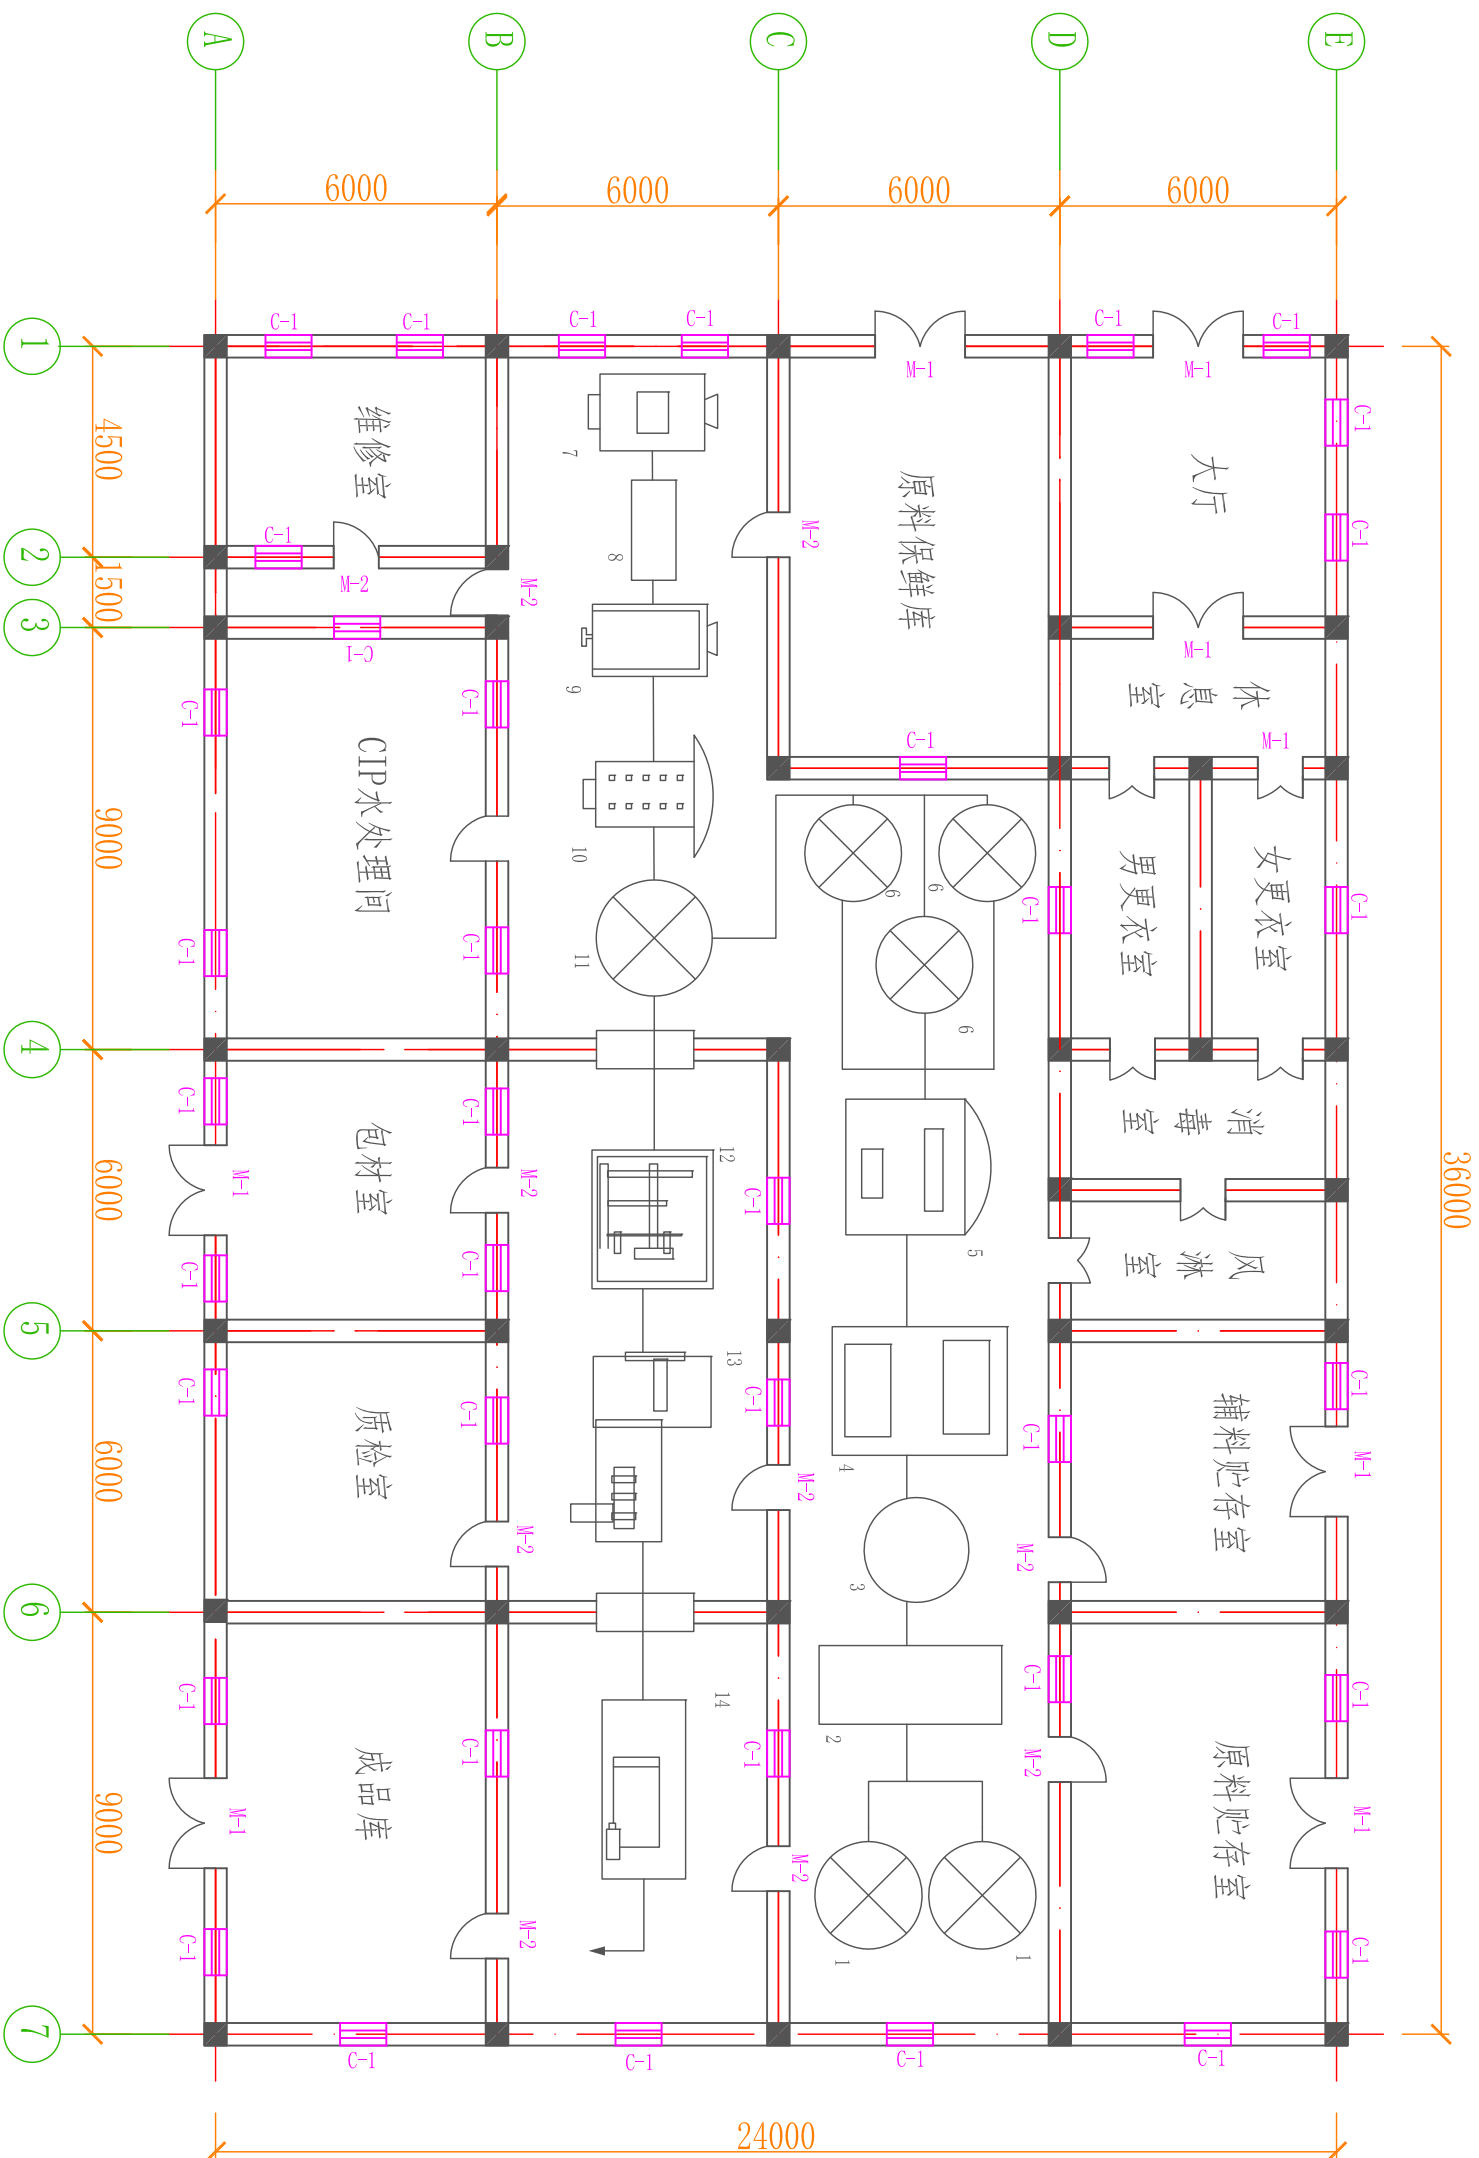

双扇门

| 序号 | 数量 | 名称     | 序号 | 数量 | 名称     |
|----|----|--------|----|----|--------|
| 1  | 2  | 储奶罐    | 8  | 1  | 带式提升机  |
| 2  | 1  | 离心净乳机  | 9  | 1  | 破碎机    |
| 3  | 1  | 标准化配料罐 | 10 | 1  | 杀菌锅    |
| 4  | 1  | 高压均质机  | 11 | 1  | 混合搅拌罐  |
| 5  | 1  | 巴氏杀菌机  | 12 | 1  | 瓶装灌装机  |
| 6  | 3  | 发酵罐    | 13 | 1  | 旋盖封盖机  |
| 7  | 1  | 蓝莓清洗机  | 14 | 1  | 全自动捆箱机 |

生产车间平面图

|    |            |       |       |
|----|------------|-------|-------|
| 学号 | 2209014301 | 比例    | 1:100 |
| 数量 | 3          | 共 3 张 | 第 2 张 |